




FB 100010-001

2

3

4

5

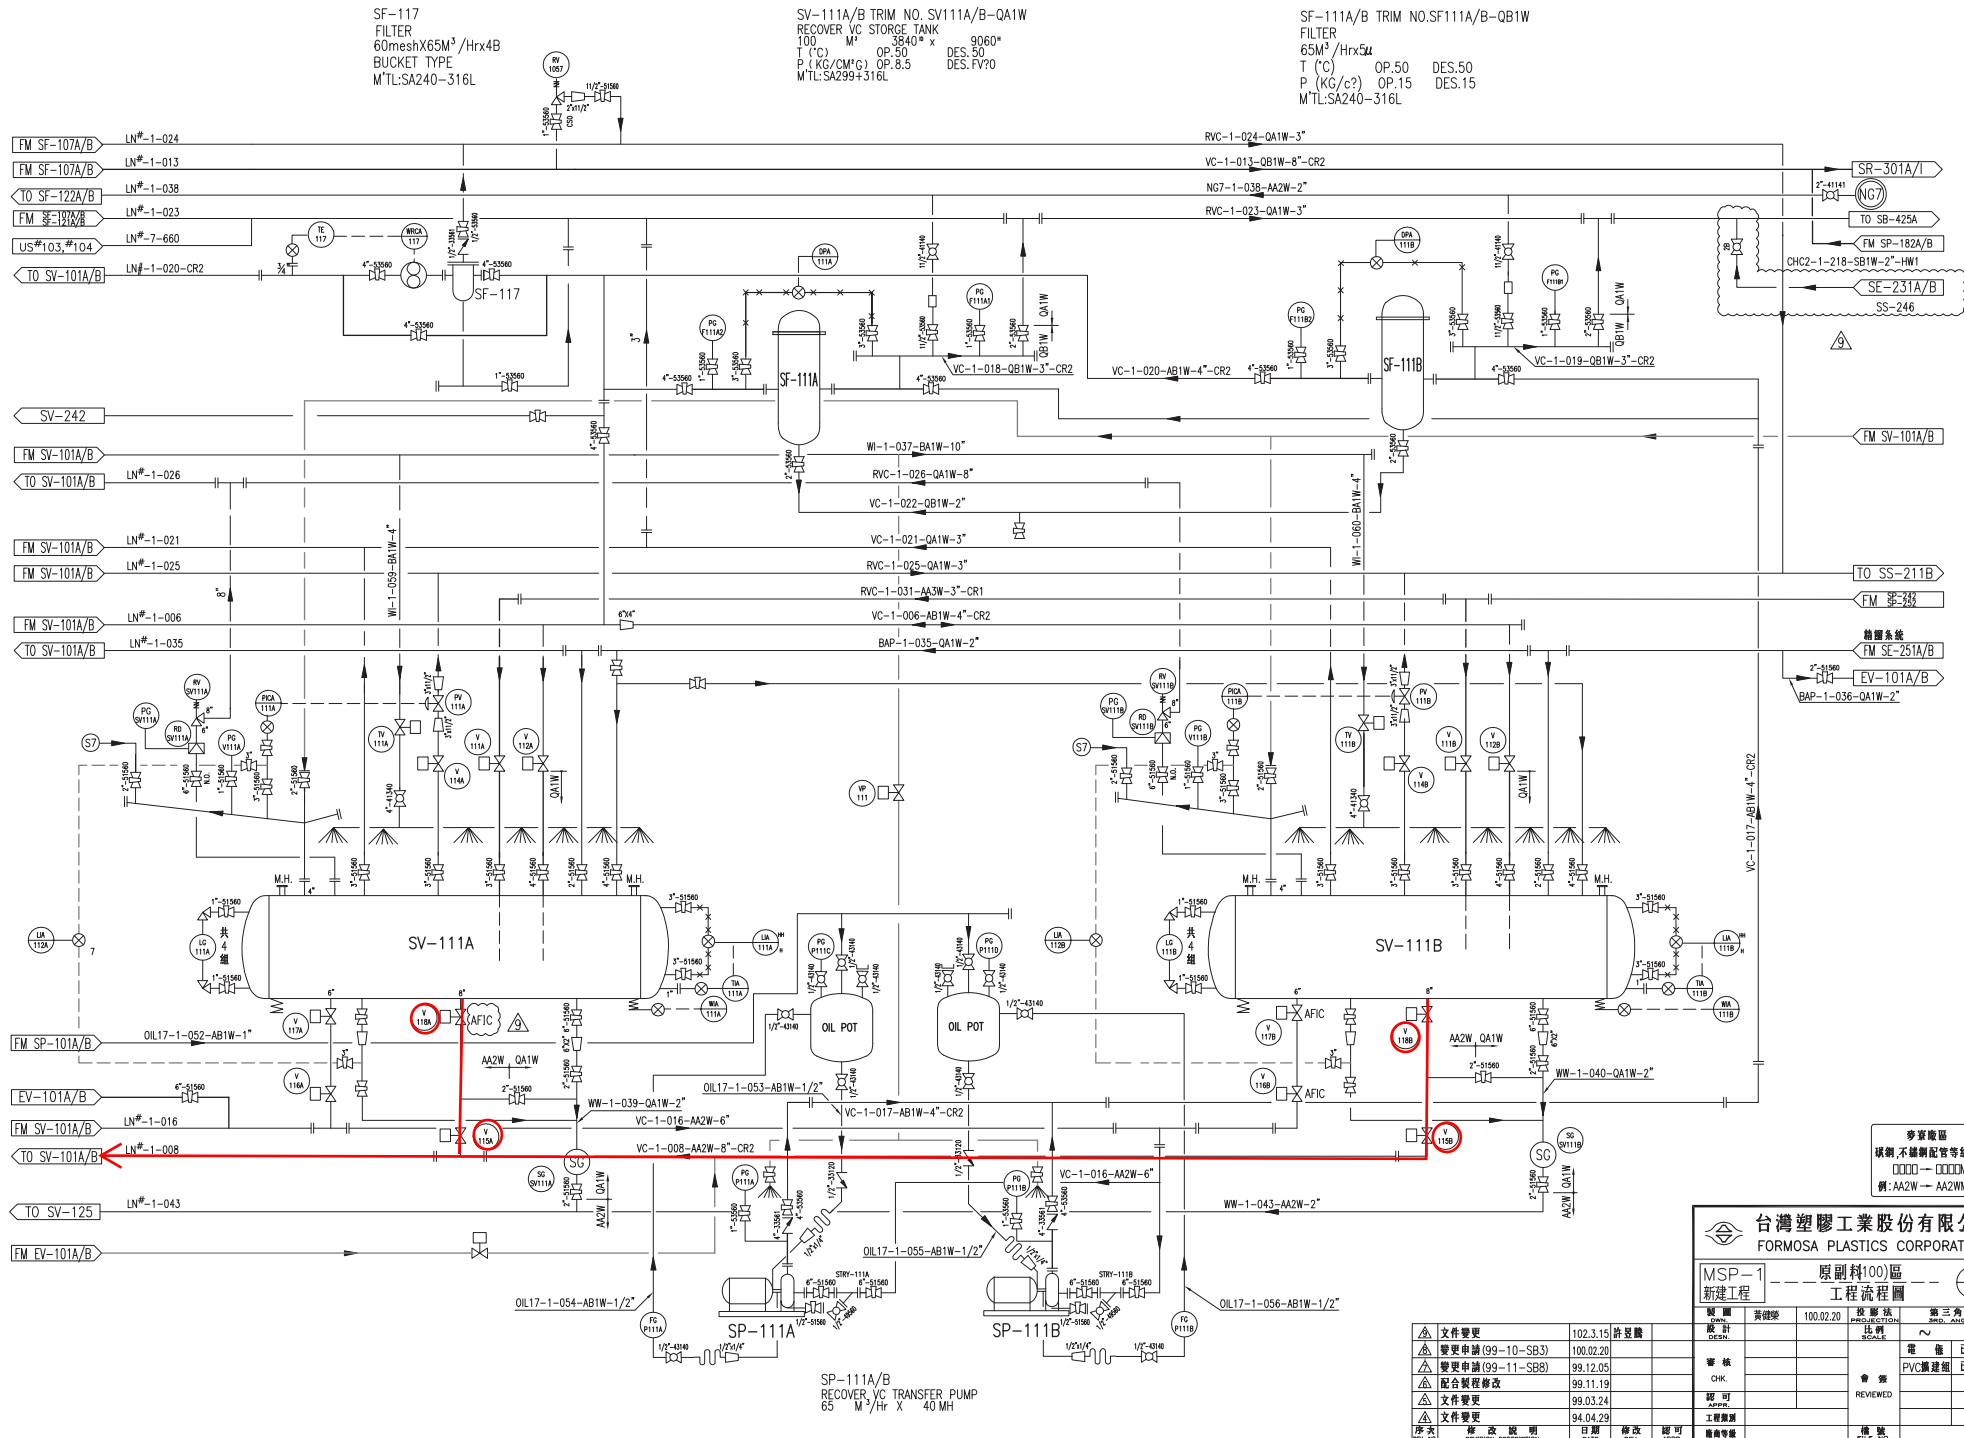


THE INFORMATION CONTAINED IN THIS DOCUMENT IS THE PROPERTY OF PPC LTD. IT IS TO BE USED FOR THE PROJECT AND NOT BE MISUSED IN ANY WAY. WRITTEN CONSENT OF PPC LTD. IS REQUIRED FOR ANY REUSE OR MODIFICATION OF THE INFORMATION. UNLESS OTHERWISE SPECIFIED, ALL DIMENSIONS ARE IN MILLIMETERS. UNLESS OTHERWISE SPECIFIED, ALL MATERIALS ARE TO BE OF THE HIGHEST QUALITY AVAILABLE.

台灣塑膠工業股份有限公司
FORMOSA PLASTICS CORPORATION

MSP-1 原料(100)區 新建工程 工程流程圖

圖名	圖號	日期	比例	第三角法
設計	100.02.20	100.02.20	1:1	電 檢 已會審
審核		99.12.05		PVC圖建組 已會審
配合製圖修改		99.11.19		電 檢 已會審
文件變更		99.03.24		電 檢 已會審
文件變更		94.04.29		電 檢 已會審
修改				電 檢 已會審

圖名	圖號	日期	比例	第三角法
設計	100.02.20	100.02.20	1:1	電 檢 已會審
審核		99.12.05		PVC圖建組 已會審
配合製圖修改		99.11.19		電 檢 已會審
文件變更		99.03.24		電 檢 已會審
文件變更		94.04.29		電 檢 已會審
修改				電 檢 已會審

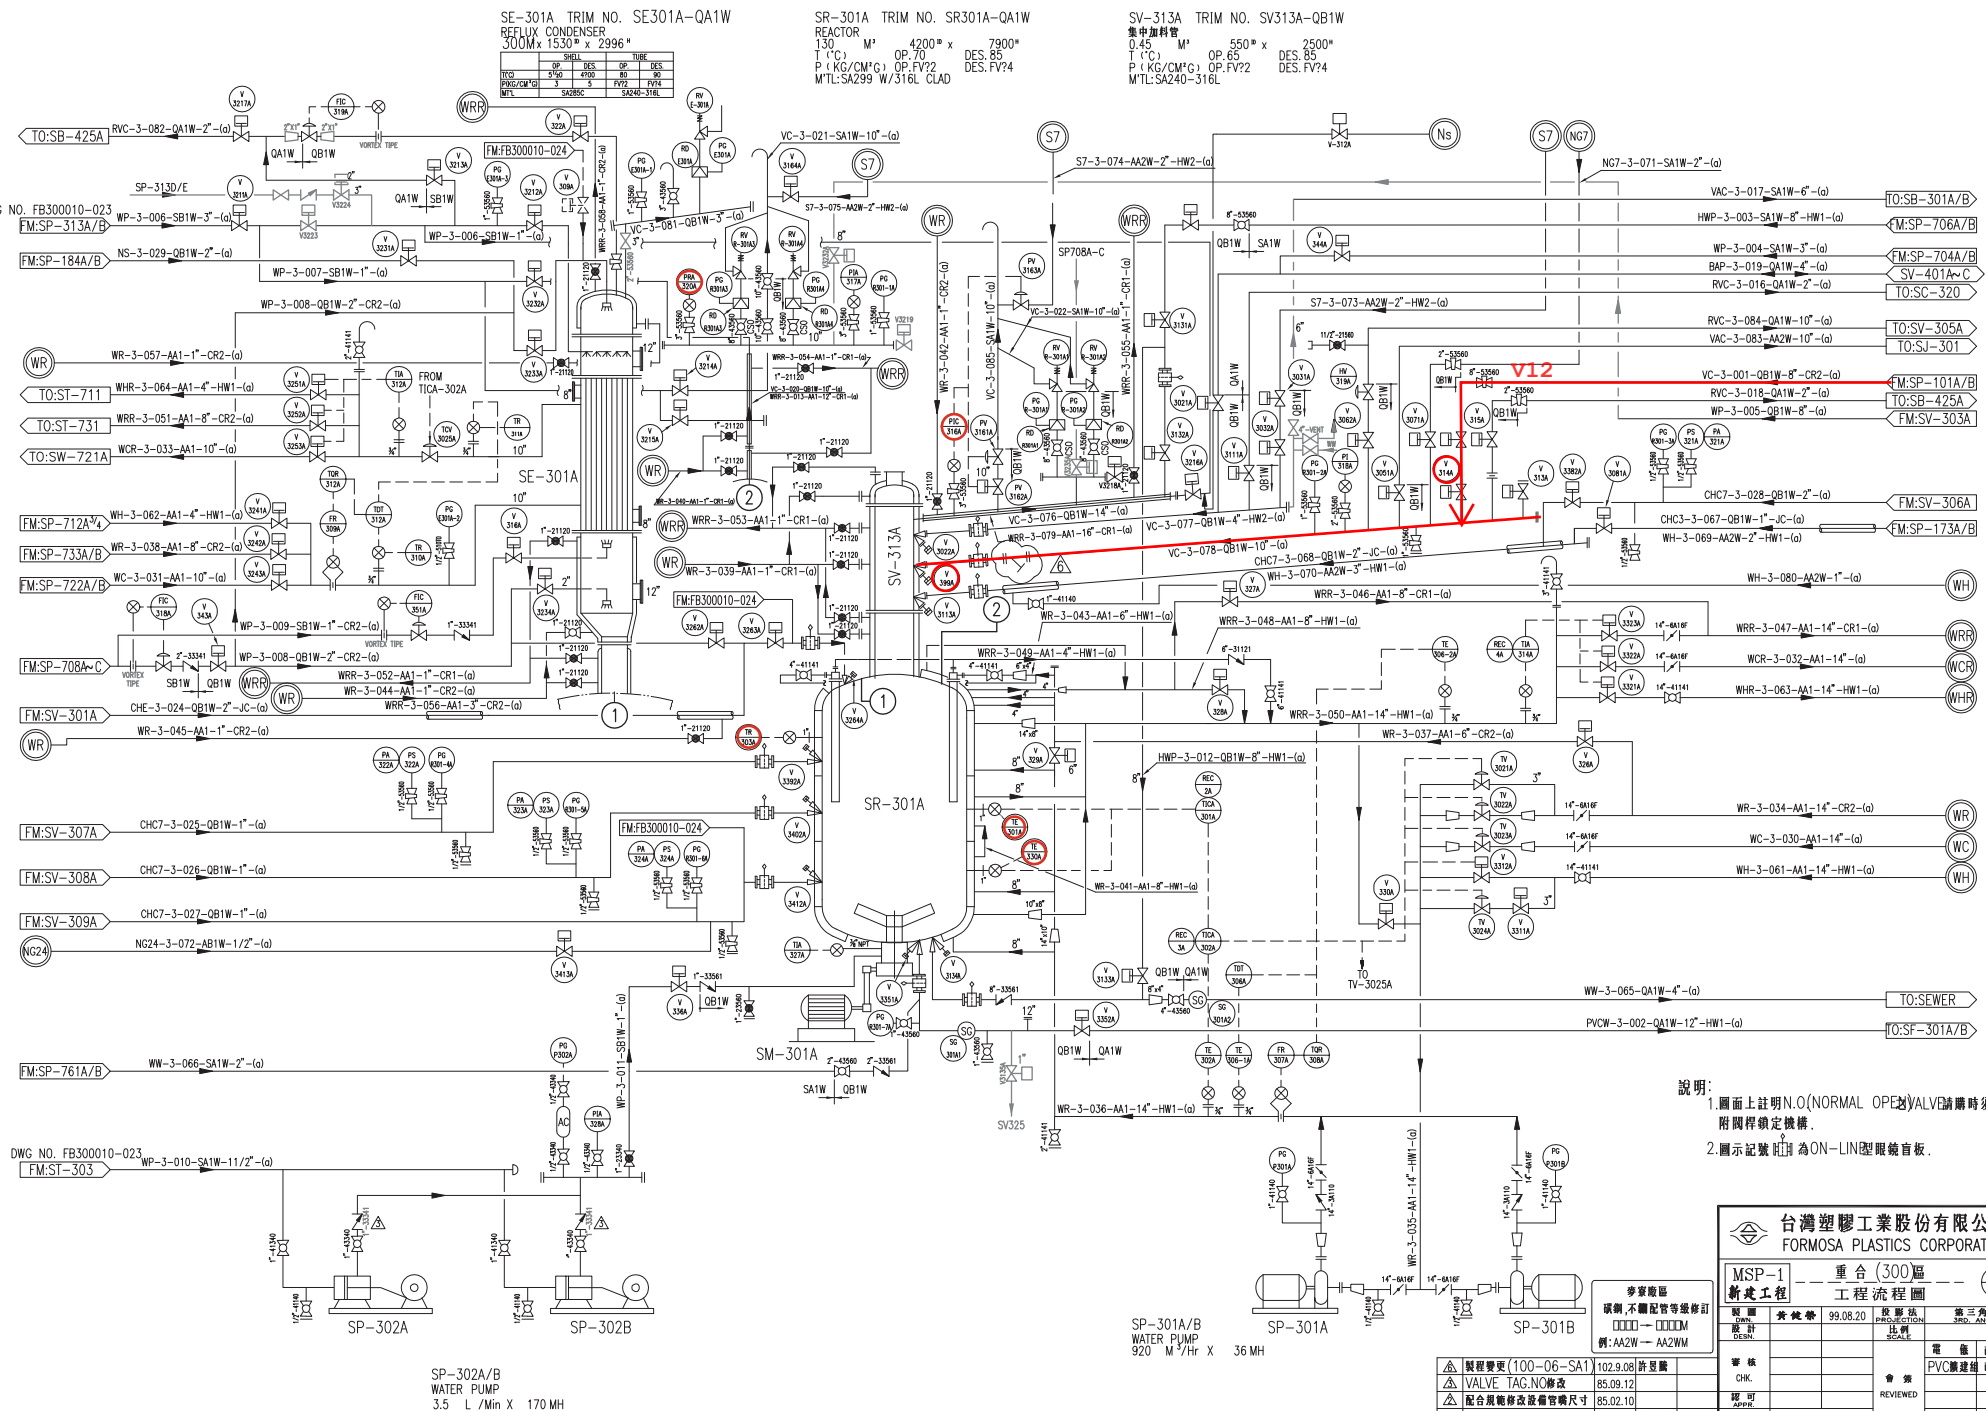

THE INFORMATION CONTAINED IN THIS DOCUMENT IS THE PROPERTY OF FPC LTD., AND IS NOT TO BE COPIED OR DISCLOSED TO THIRD PARTIES WITHOUT THE PRIOR WRITTEN CONSENT OF FPC LTD., NOR IS IT TO BE MISUSED IN ANY WAY.

此等文件之內容為聯公司財產，未經聯公司或聯公司之董事或經理人書面許可，不得複印或向任何第三者或任何方面方式施用。

說明:

- 1.圖面上註明N.O(NORMAL OPEN)之VALVE請開時須要求
附閥鎖定機構。
- 2.圖示記號(ON-LIN)為ON-LIN型眼鏡盲板。

FORMOSA PLASTICS CORPORATION						REV'D	
						FORMOSA PLASTICS CORPORATION	
MSP-1 新建工程	重合(300厘)				(11) 32		
工程流程图							
概圖 DESIGN	基礎梁	99.08.20	設廠計畫 SCALE	第三角法 ISO_ANGLES			
審核 CHK.			會 簽 REVIEWED	電 腦 PVC繪建檔	已會審 日會審	專 人 第一工務課	
認可 APPH						PVC工程師 2	
工程預算						PVC技師 2	
廠商估價							
傳 真				91GAM473-01			